




20 x 10 ft corner booth / speculative exhibition design

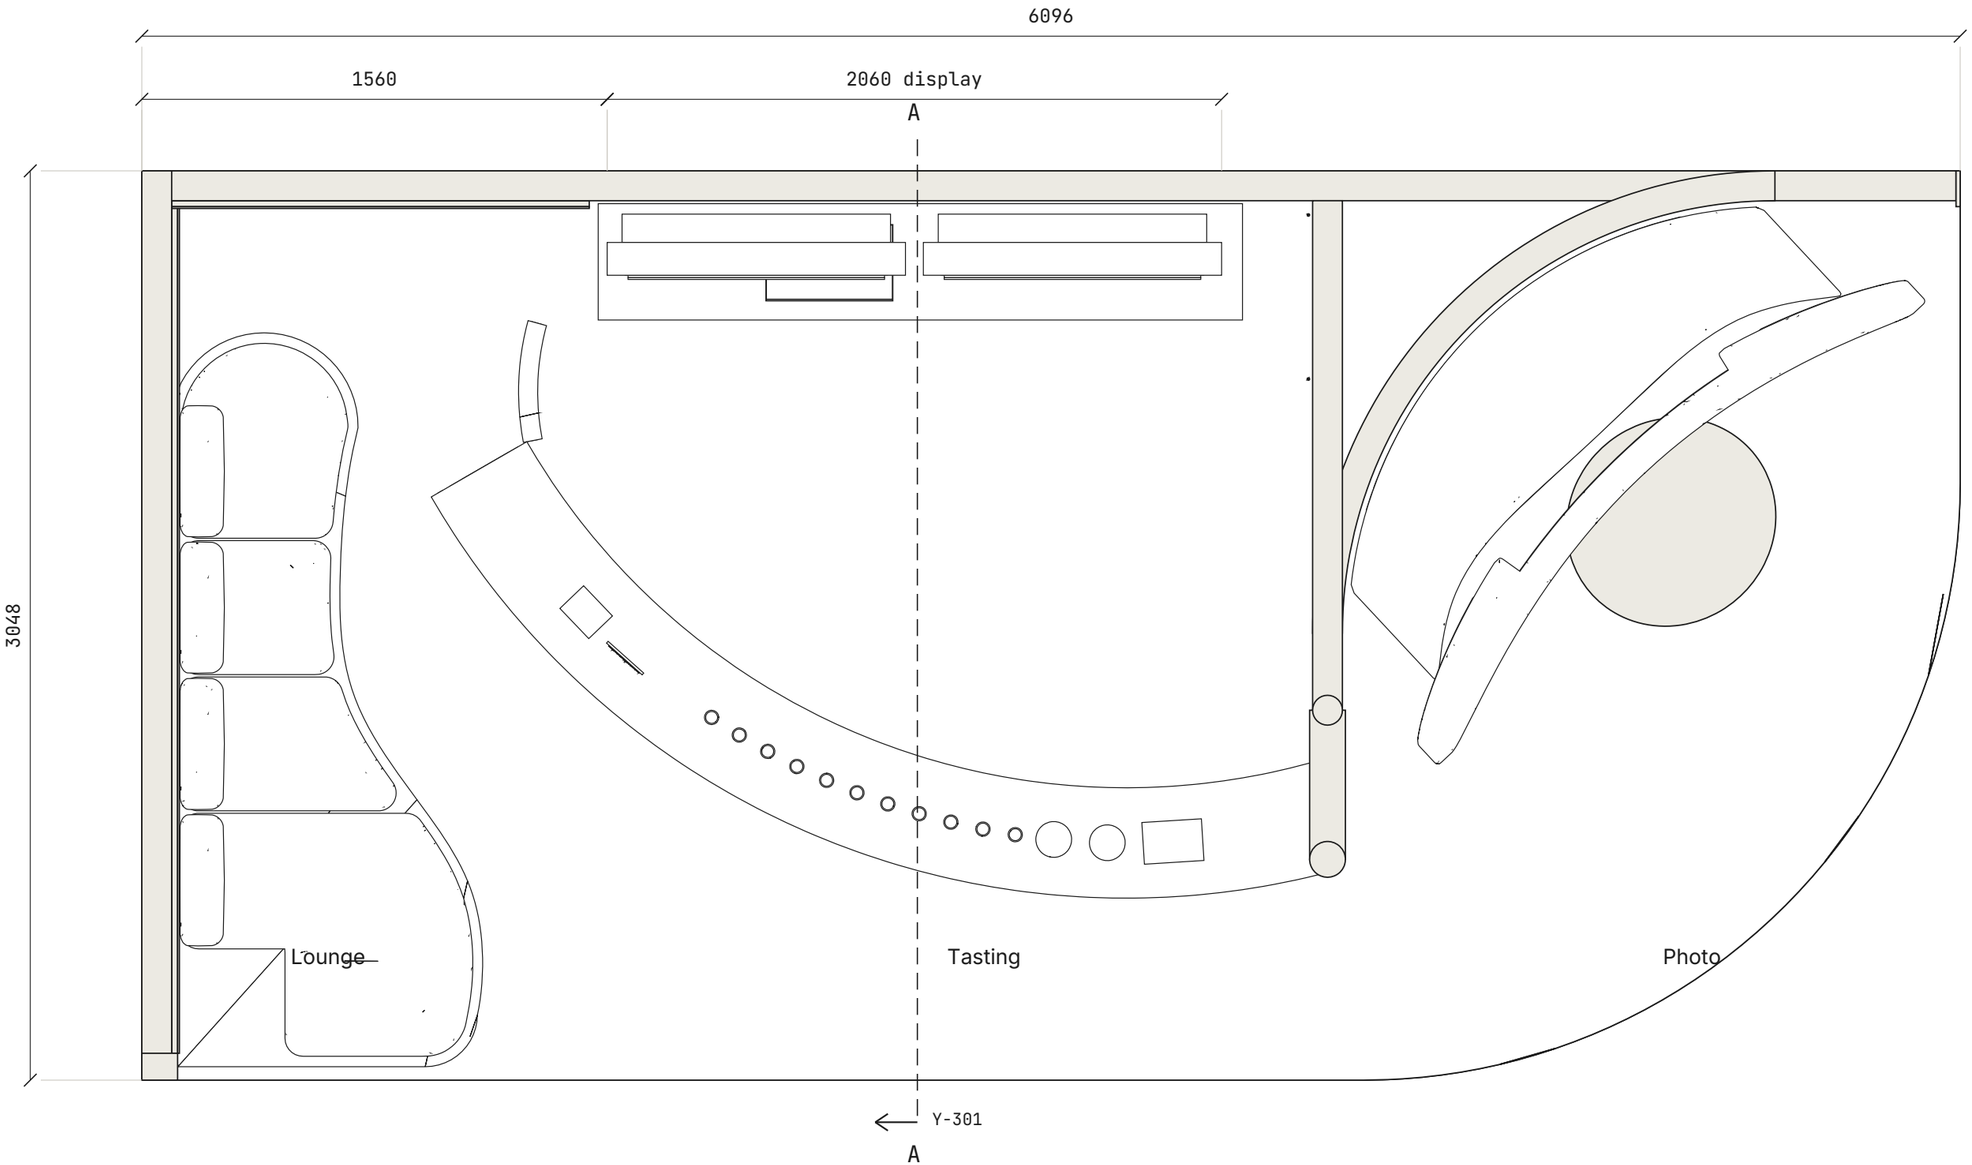



0 1000 mm

1:20 / Planting and small props omitted

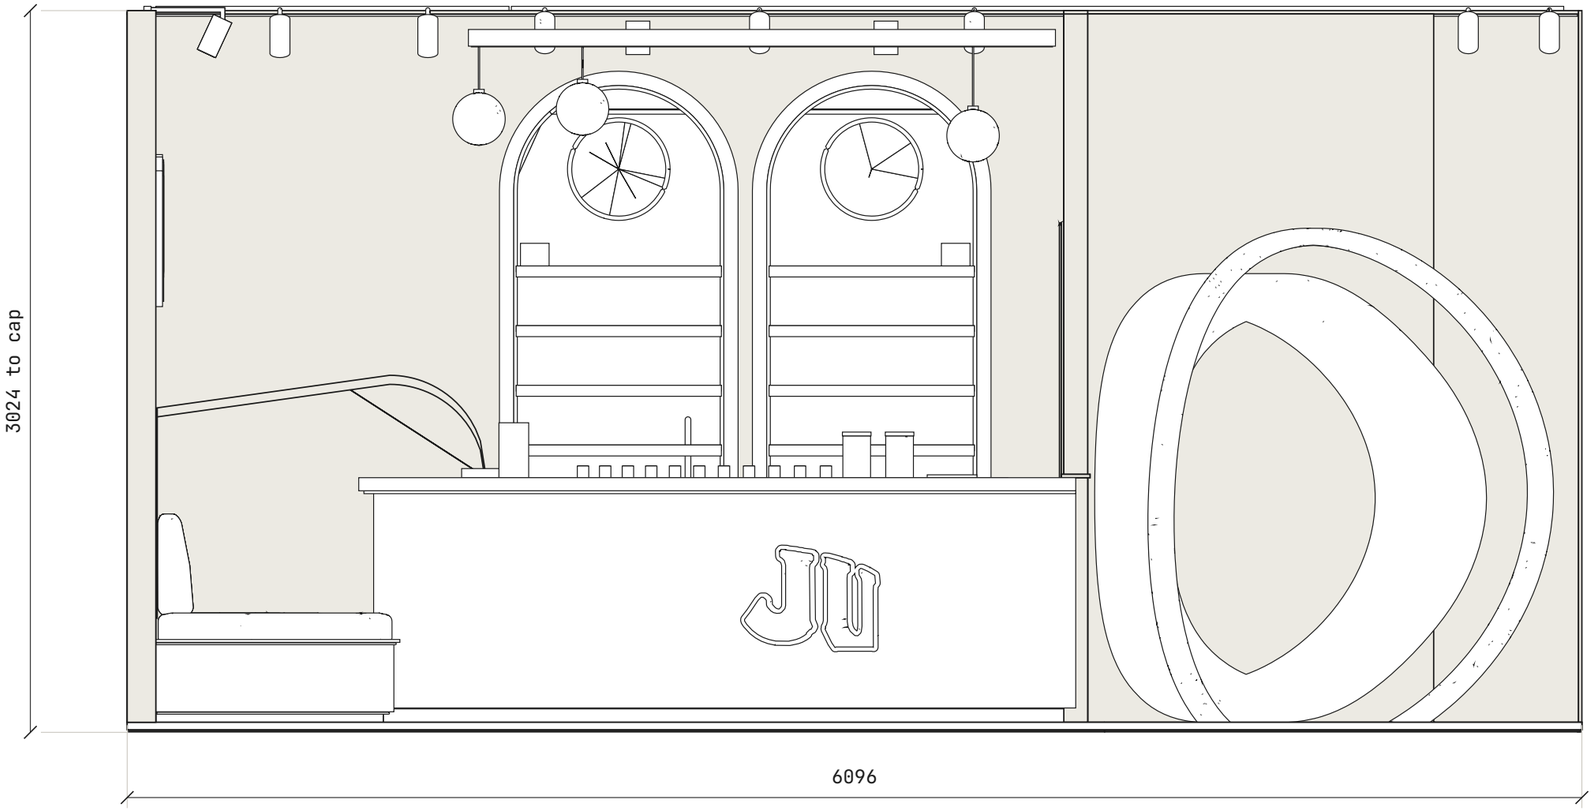


Front / 1:25

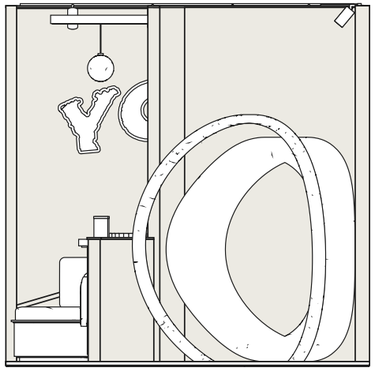

Right / 1:50


+3012 Track

+2994 Wall cap


+12 Finished floor

-30 Hall floor

Datum levels in model coordinates; planting omitted.

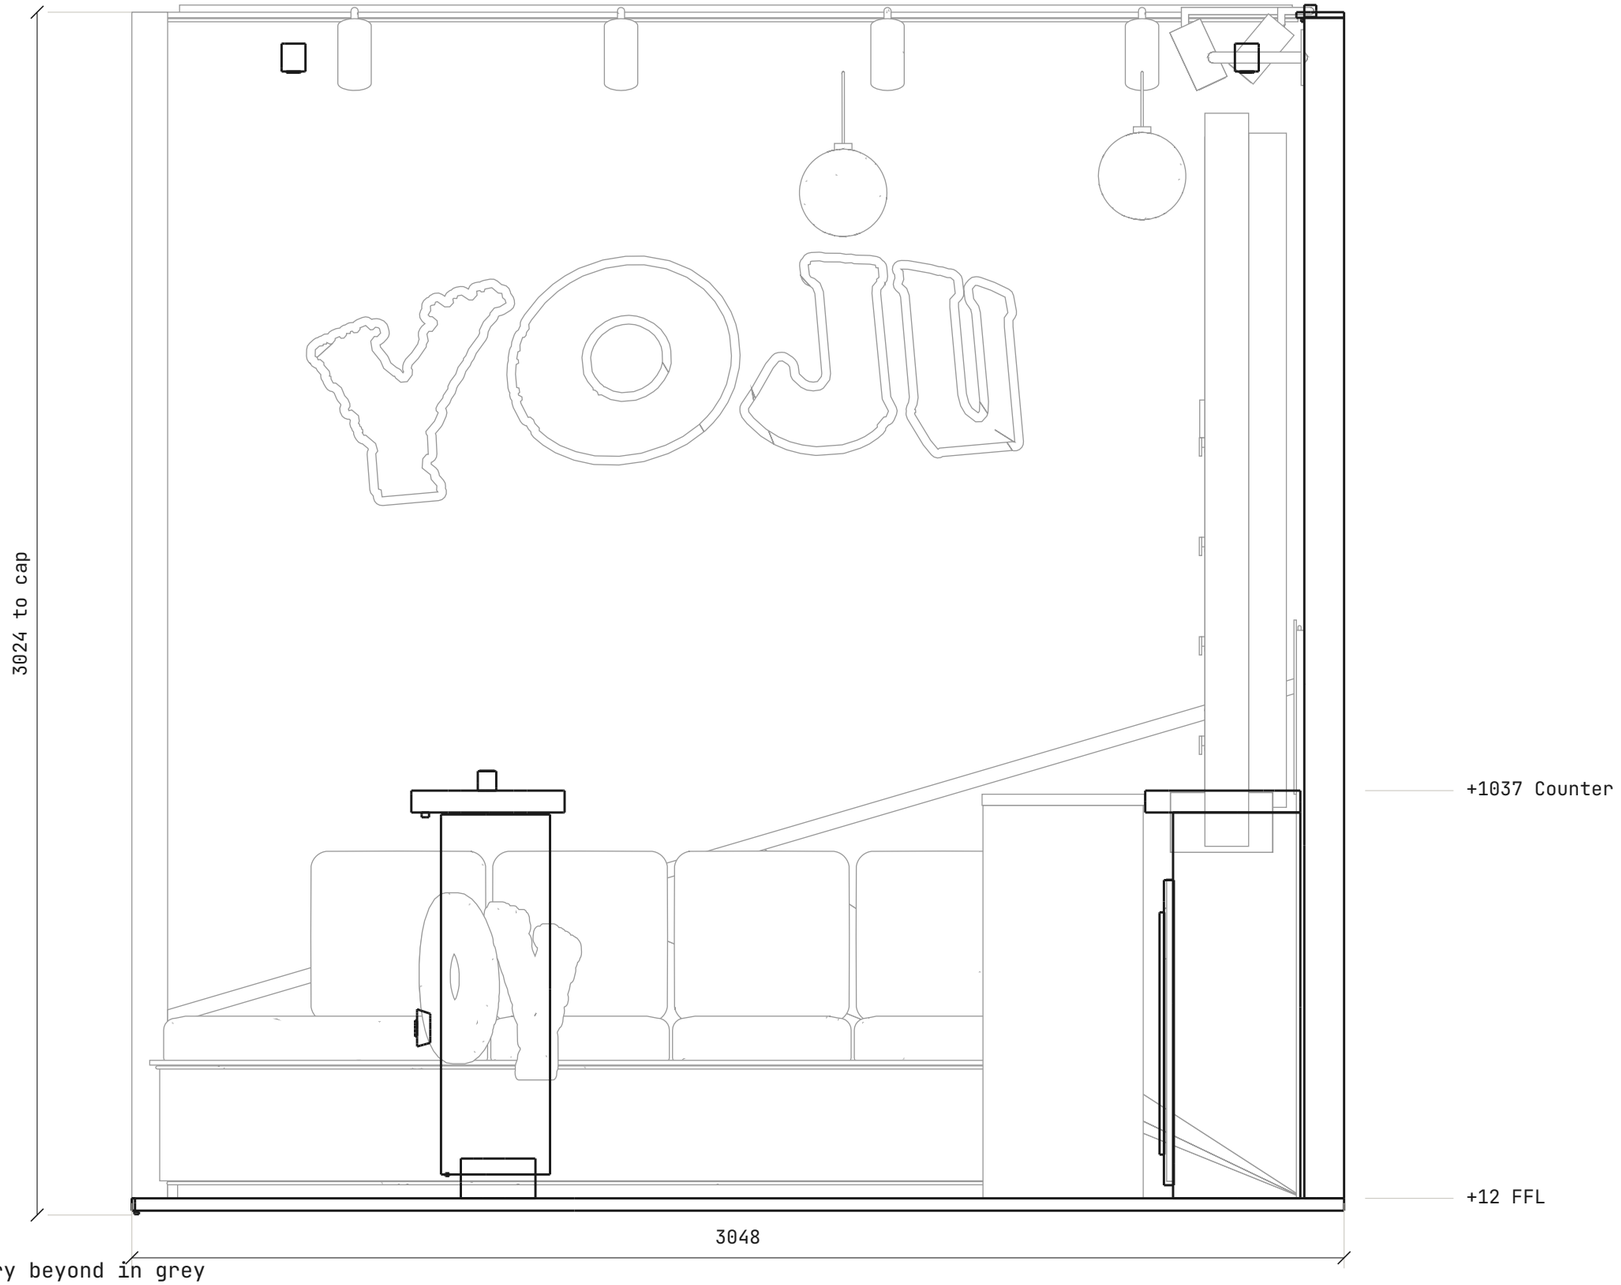



1:15 / Cut at X = 2600 / Geometry beyond in grey

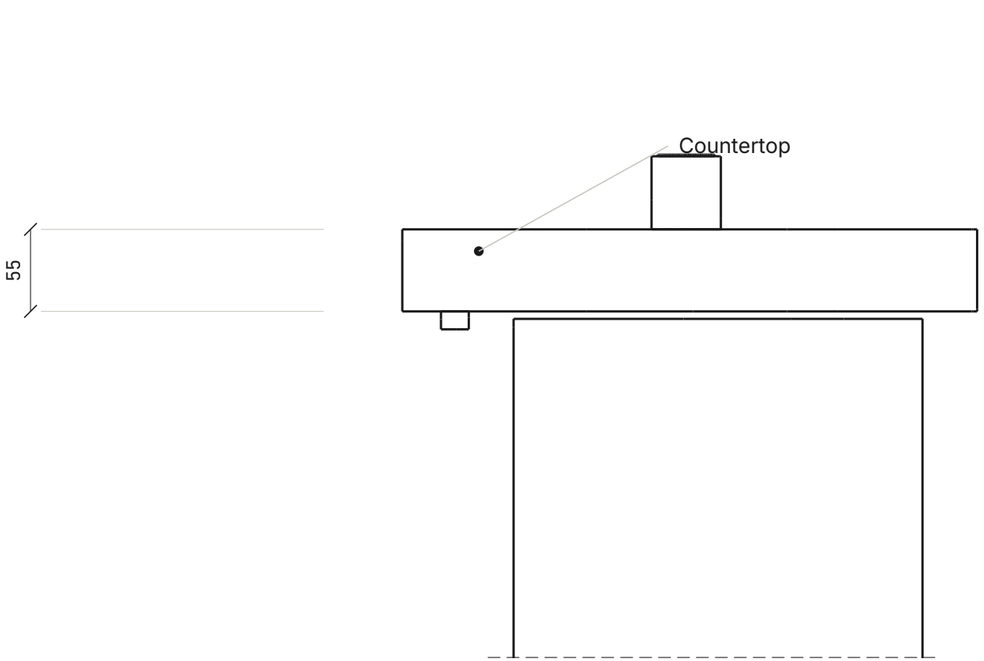


Bar edge / 1:4

Counter and cabinet shells


Model sections / substrate, joints and fixings to develop

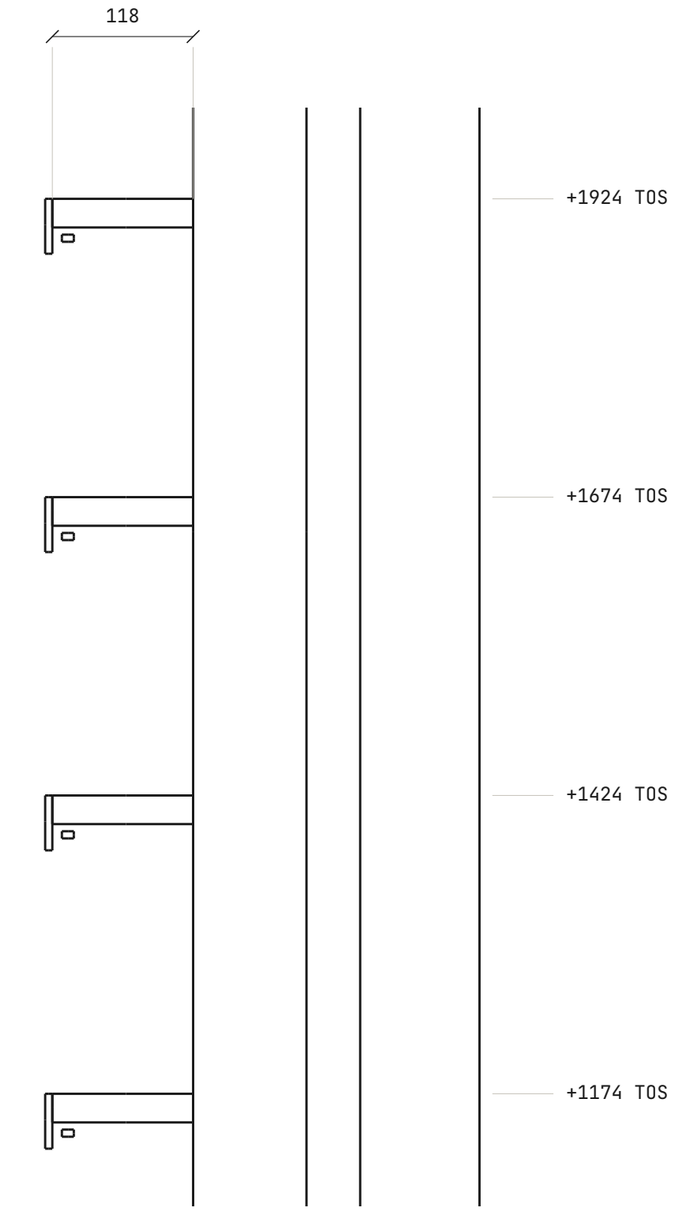


Display / 1:5

# YOJU / Overhead lighting layout

DEYING CHEN

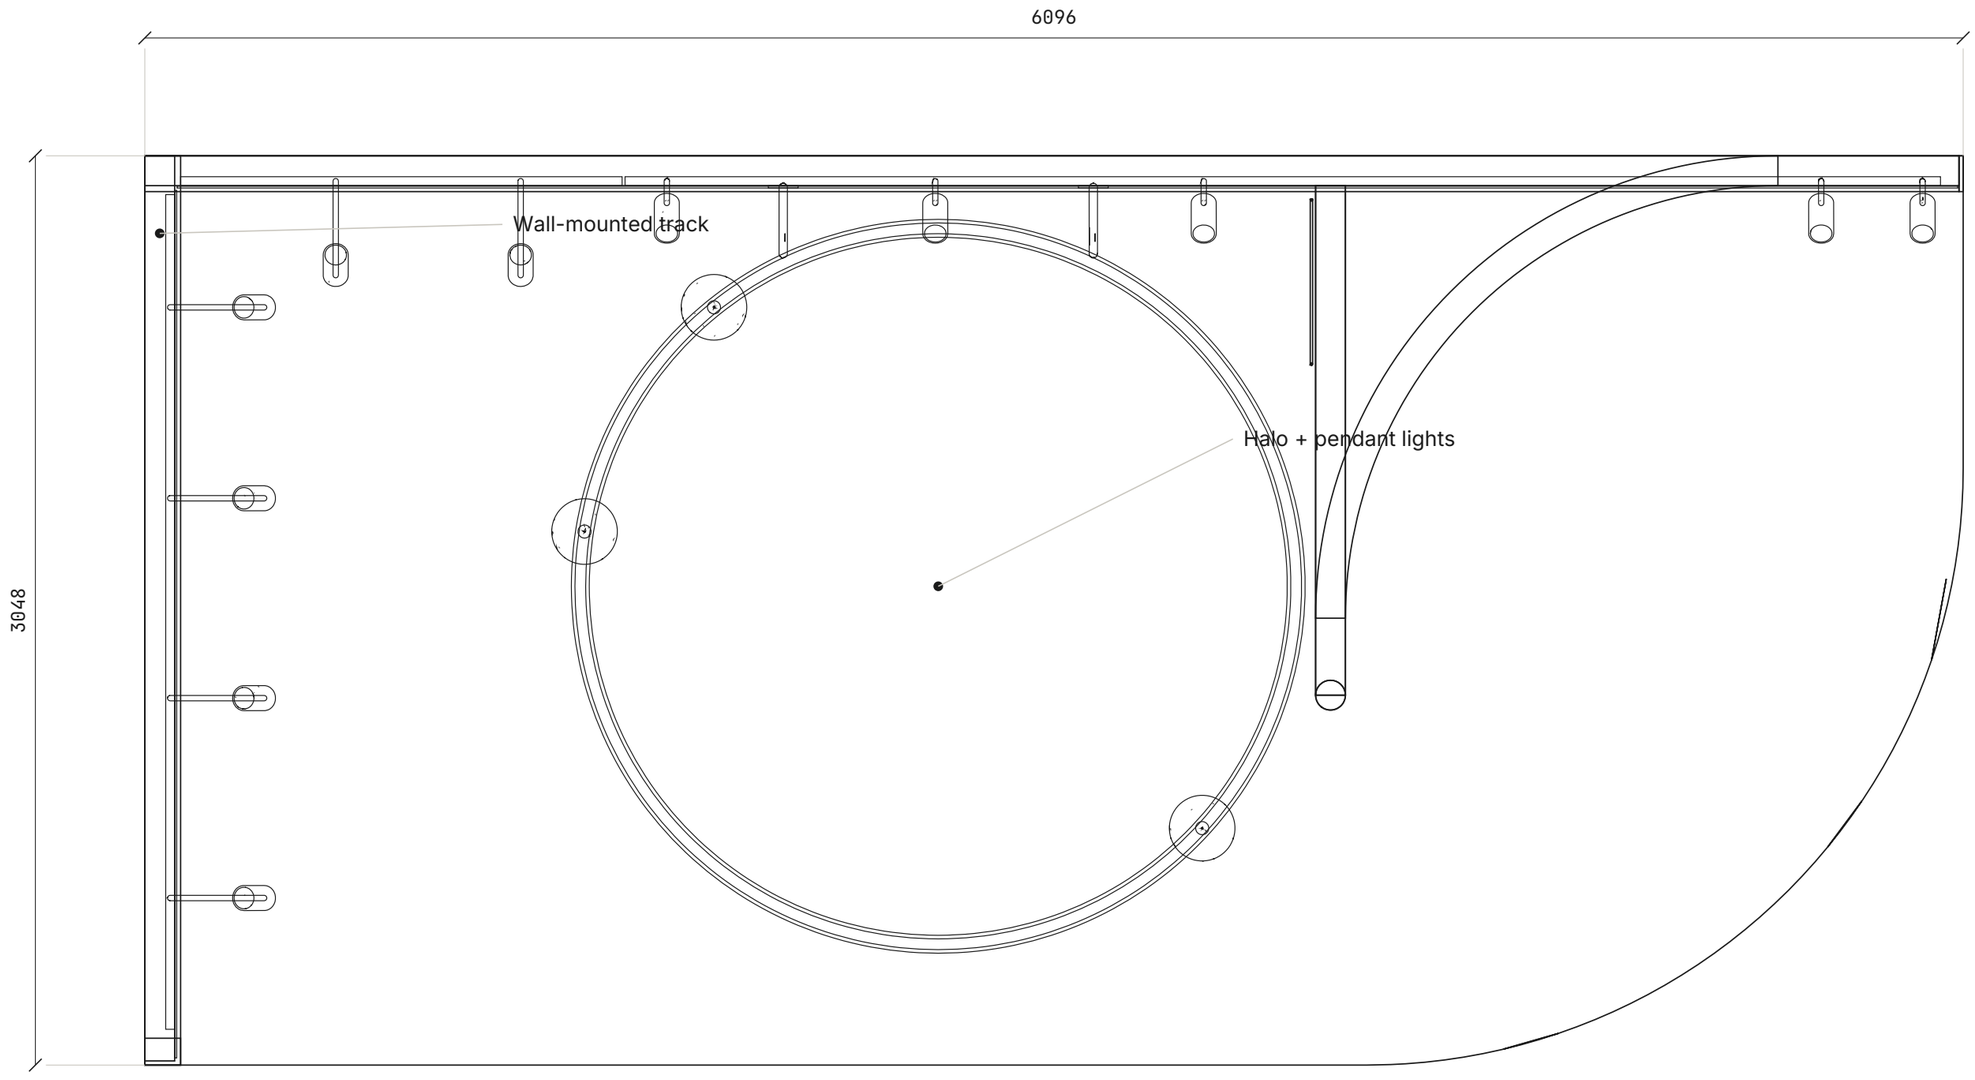


1:20 / Geometry layout; electrical routing to coordinate